

RECORD OF SURVEY NO. 2469 BOUNDARY LINE ADJUSTMENT EXHIBIT B

MBR 10889

A PORTION OF SECTION 25, T. 11 N., R. 7 E., M.D.M.
COUNTY OF PLACER
JANUARY, 2004
ASSOCIATED LAND CONSULTANTS
FOLSOM, CA
SHEET 1 OF 3

SURVEYOR'S STATEMENT:

THIS MAP CORRECTLY REPRESENTS A SURVEY
MADE BY ME OR UNDER MY DIRECTION IN CONFORMANCE
WITH THE REQUIREMENTS OF THE LAND SURVEYORS ACT
IN SEPTEMBER, 2001 AT THE REQUEST OF KEN ANDERSON.

Fred Blomquist
FRED BLUMQUIST LS 4268
EXPIRES 6-30-04




COUNTY SURVEYOR'S STATEMENT

THIS MAP HAS BEEN EXAMINED IN
ACCORDANCE WITH SECTION 8766 OF THE
LAND SURVEYOR'S ACT THIS 6TH DAY OF
FEB. 2004.

DATED _____

VESLEY K. ZICKER RCE 31160
COUNTY SURVEYOR EXP. 6-30-04

Charles B. Grant
DEPUTY 256158

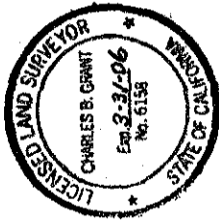


RECORDER'S STATEMENT

FILED THIS 10th DAY OF FEBRUARY 2004 AT
9:10 A.M. IN BOOK 18 OF SURVEYS AT PAGE 2
AT THE REQUEST OF ASSOCIATED LAND CONSULTANTS.

FILE NO. 2004-14020
FEE: \$14.00

Jim McCauley
JIM MCCAULEY BY *Janet J. D'Amore*
COUNTY RECORDER DEPUTY

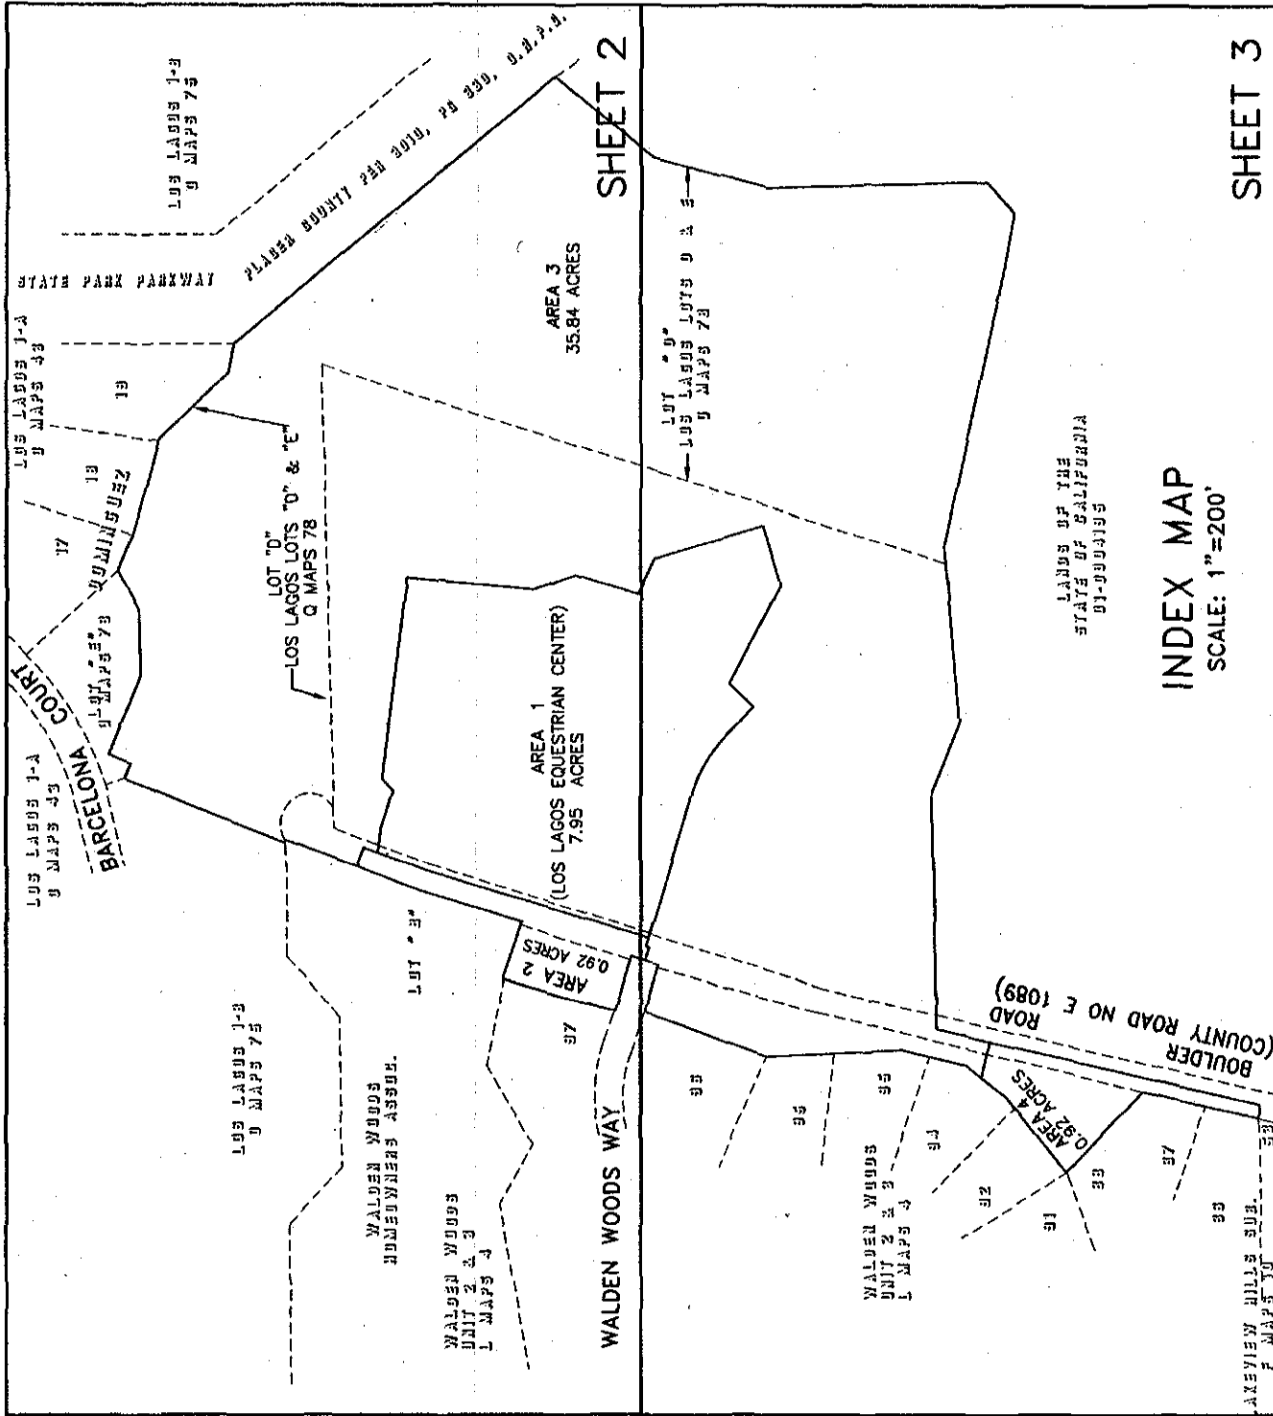

LANDS OF THE
STATE OF CALIFORNIA
91-9999195

INDEX MAP
SCALE: 1"=200'

